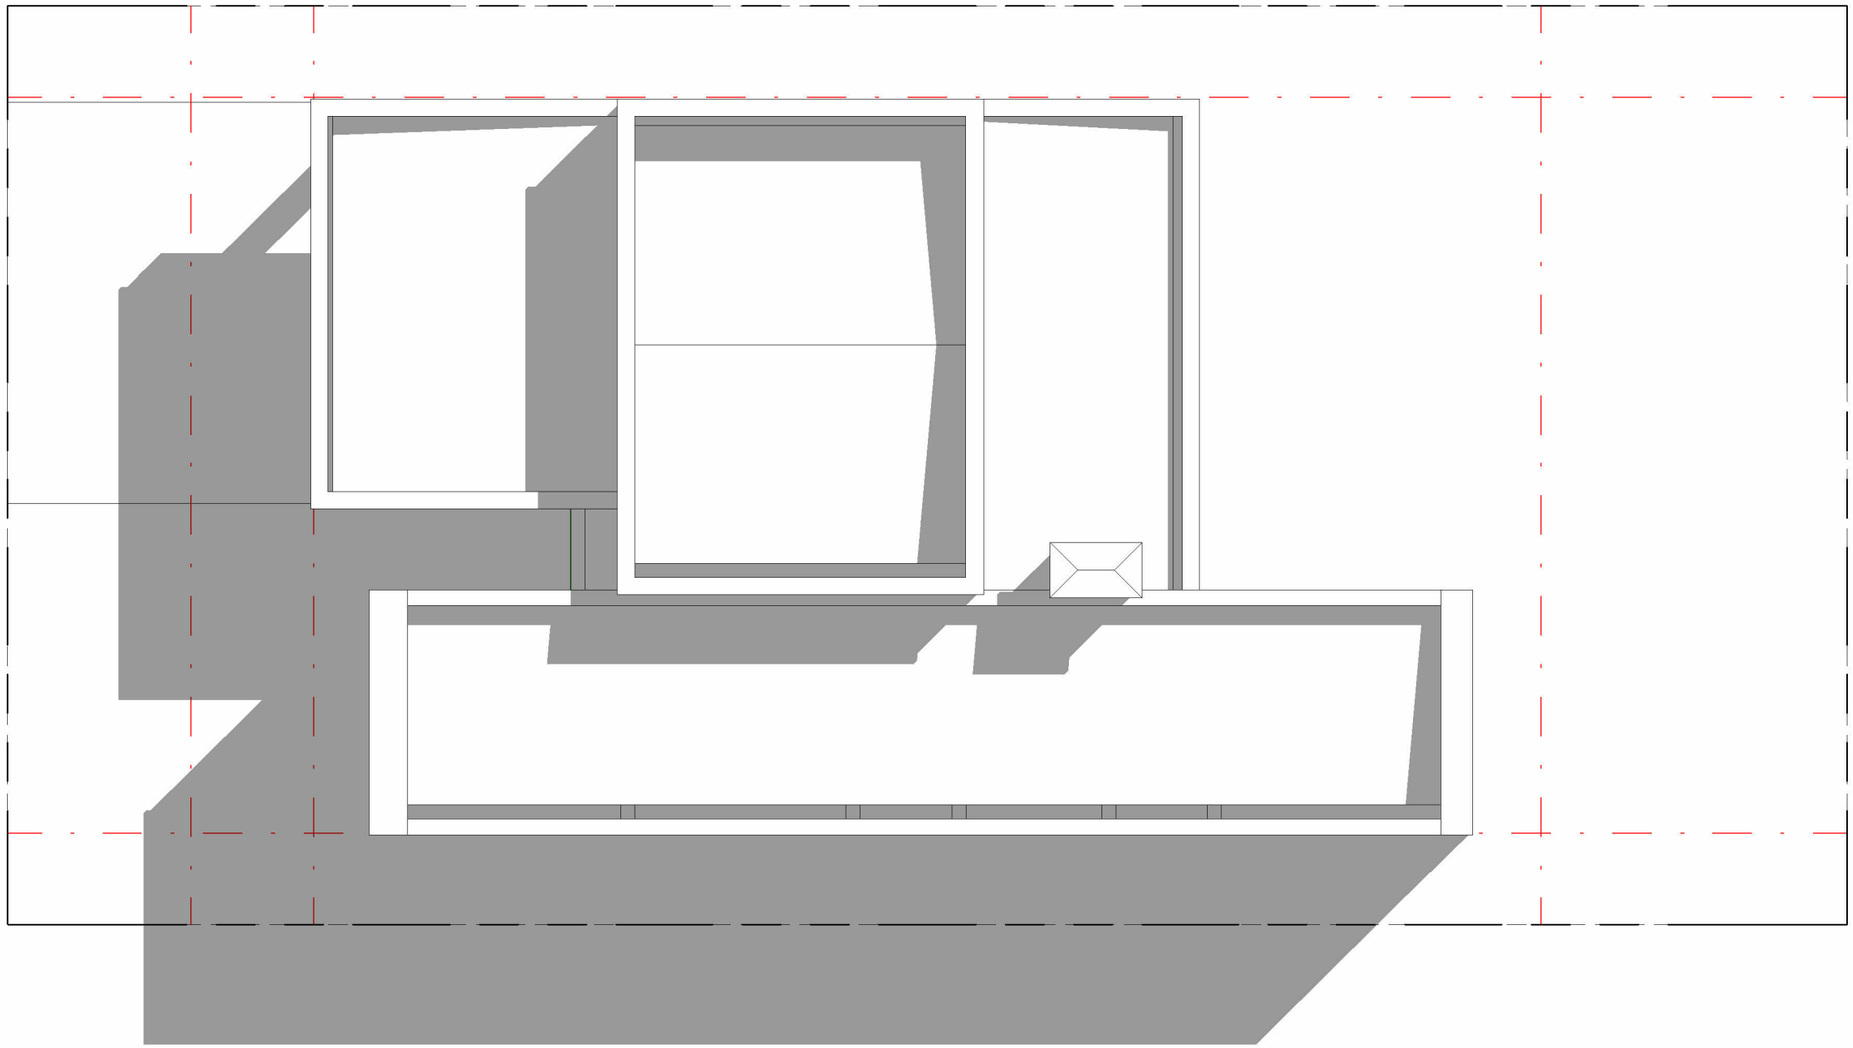
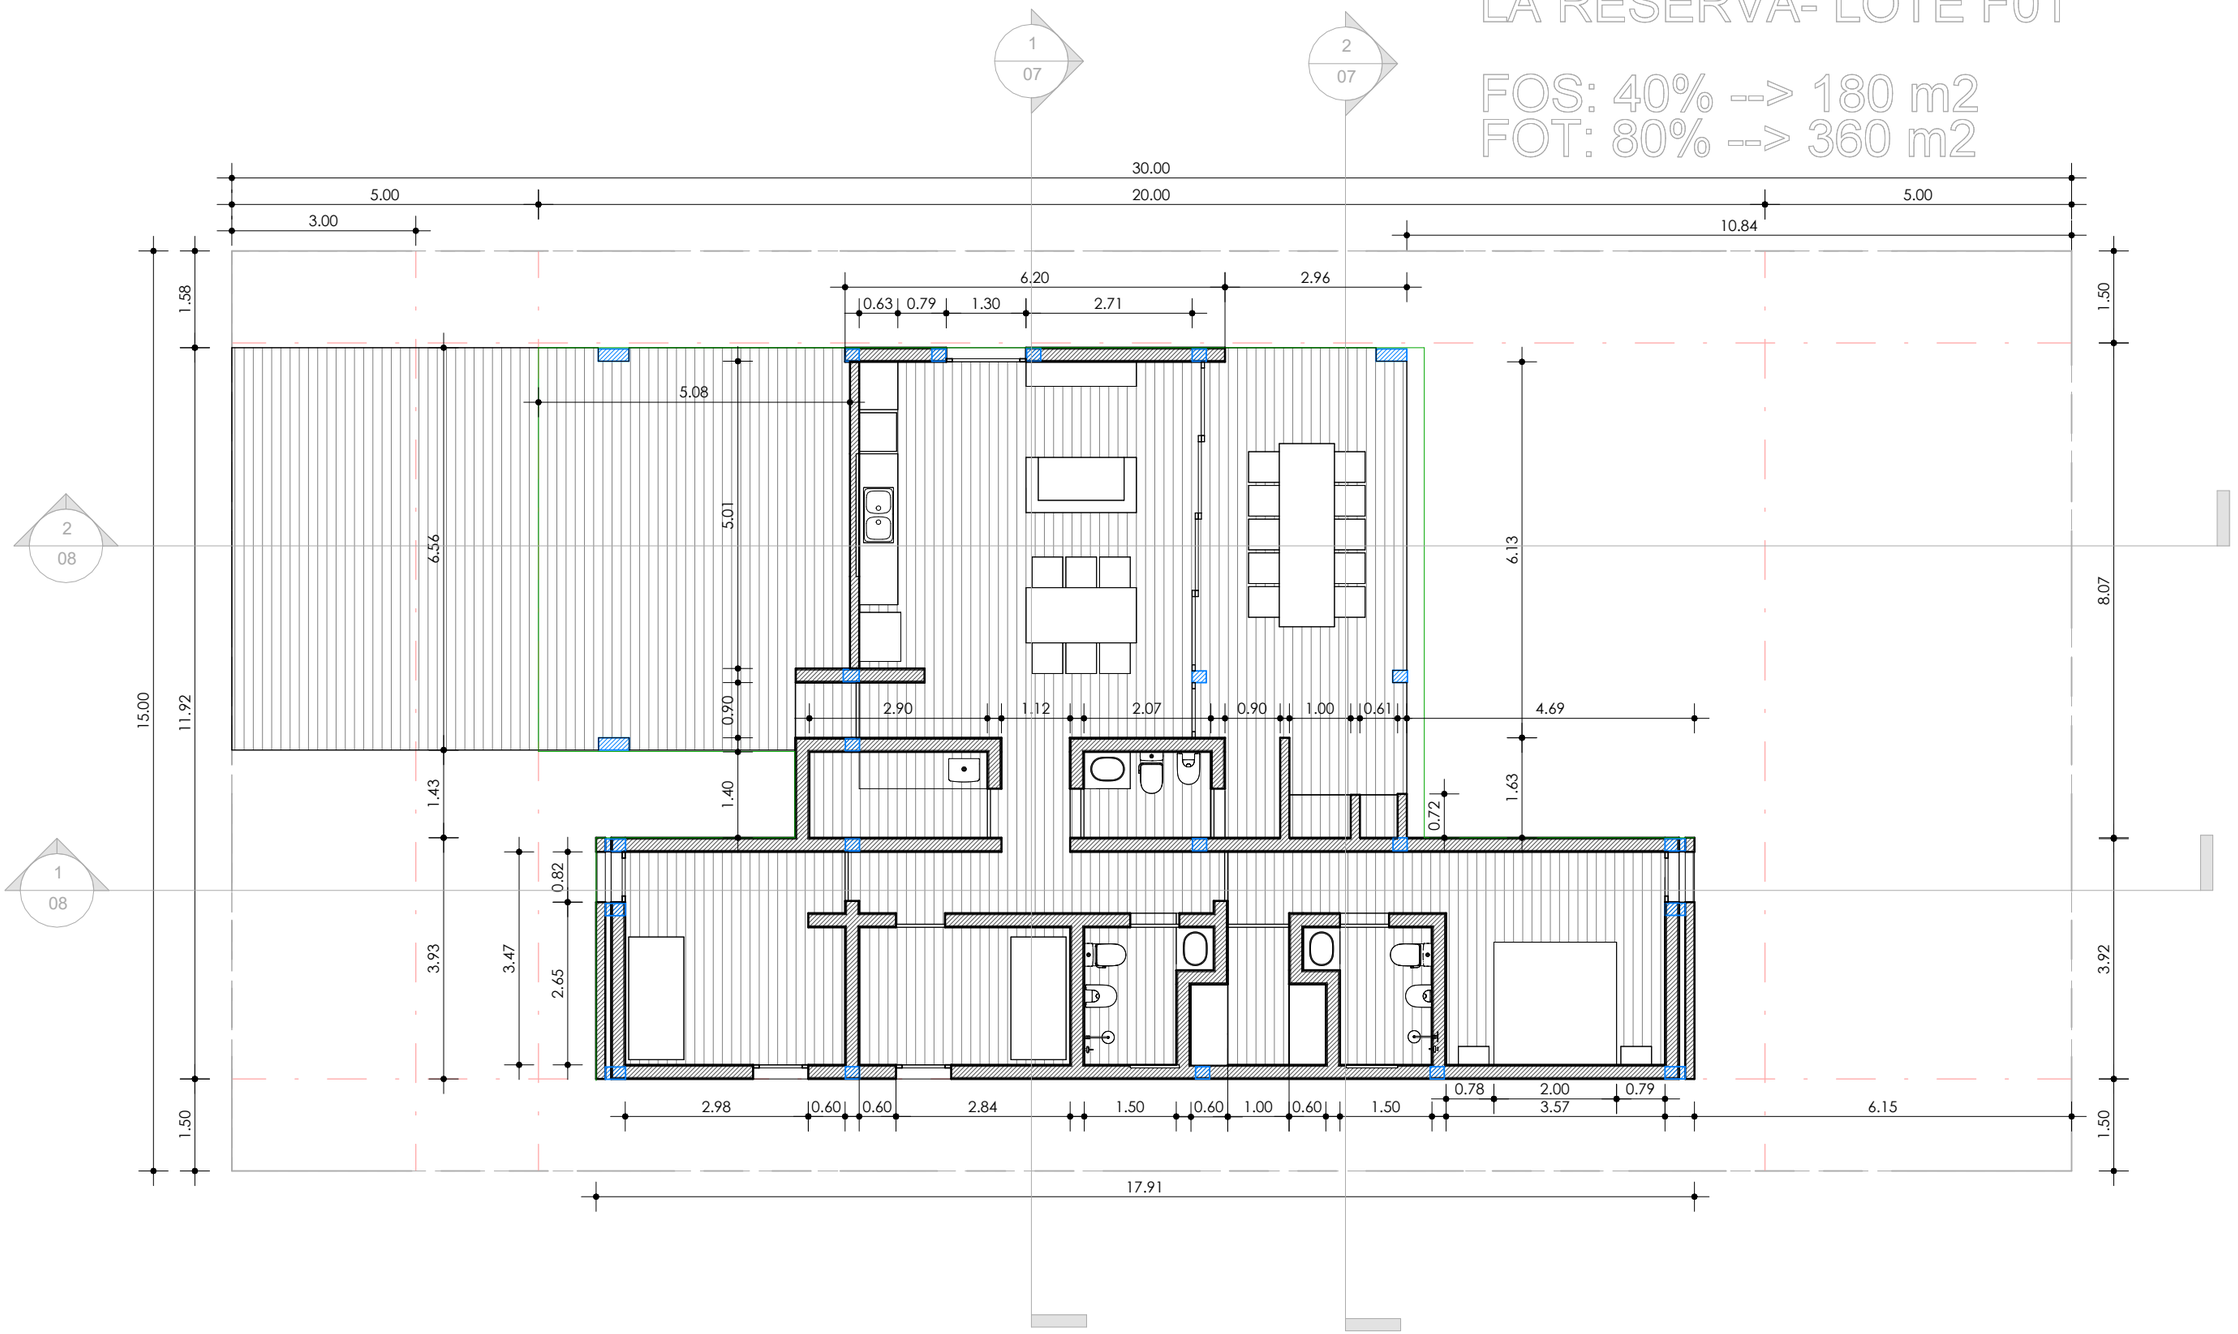
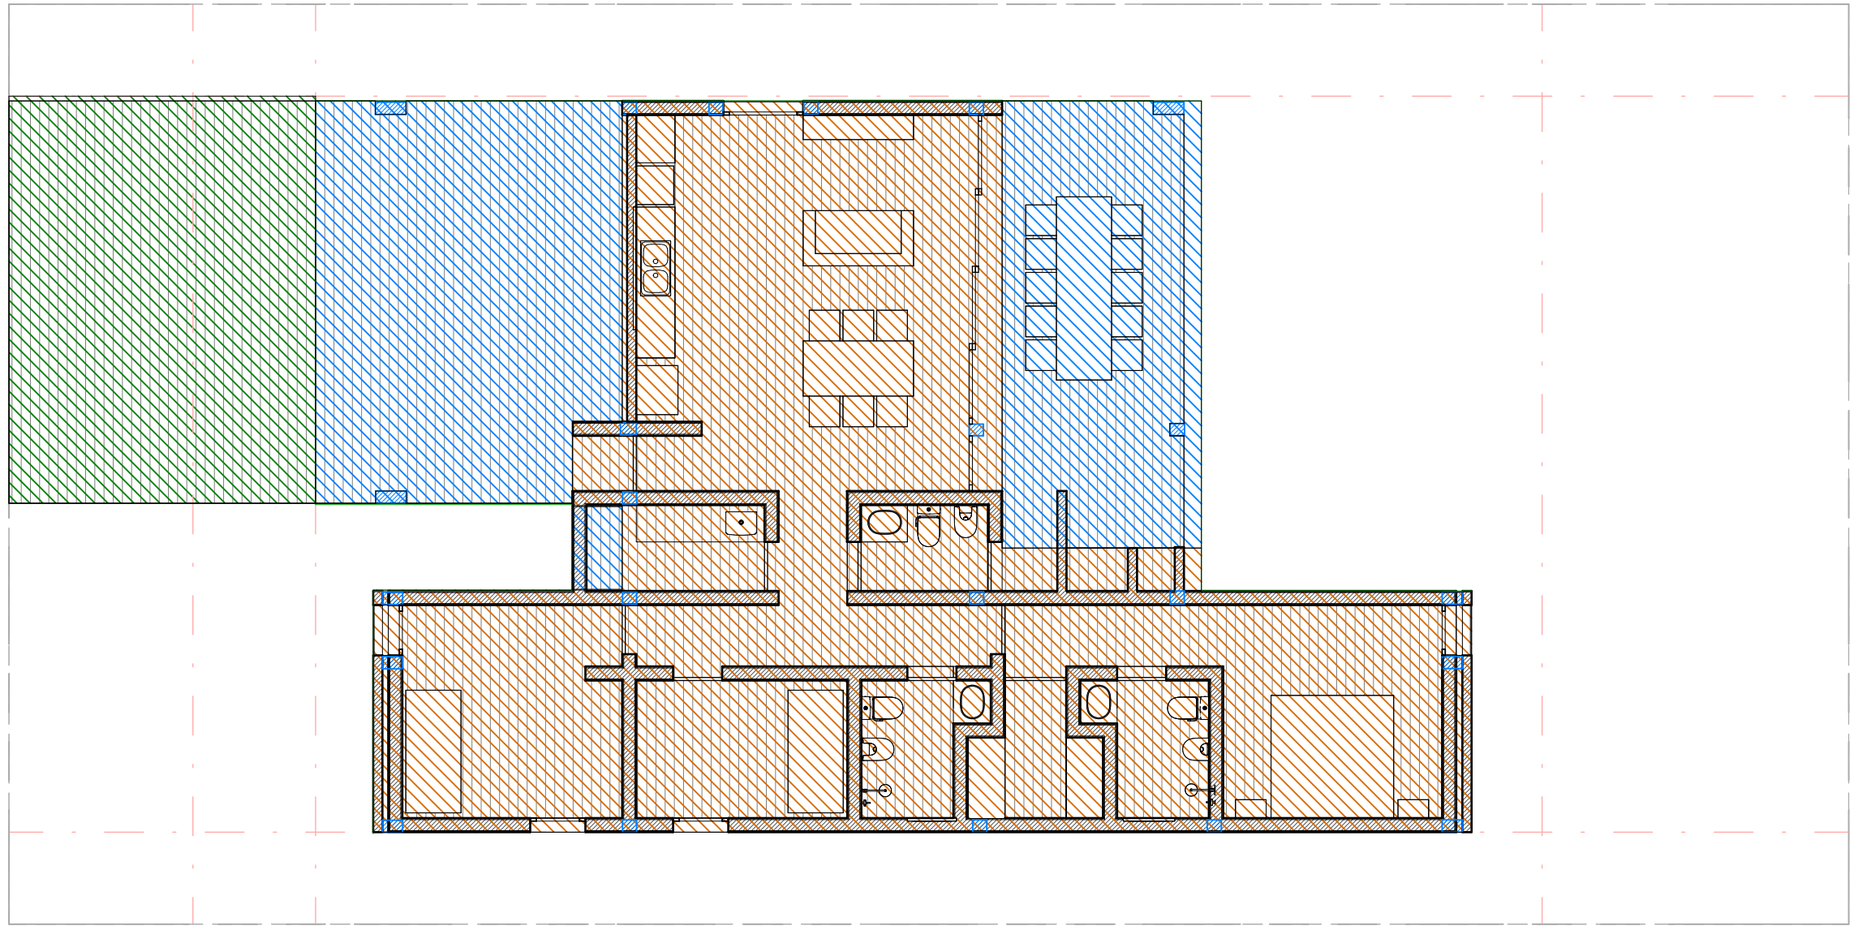

FIAT



LA RESERVA- LOTE F01

FOS: 40% --> 180 m2
FOT: 80% --> 360 m2

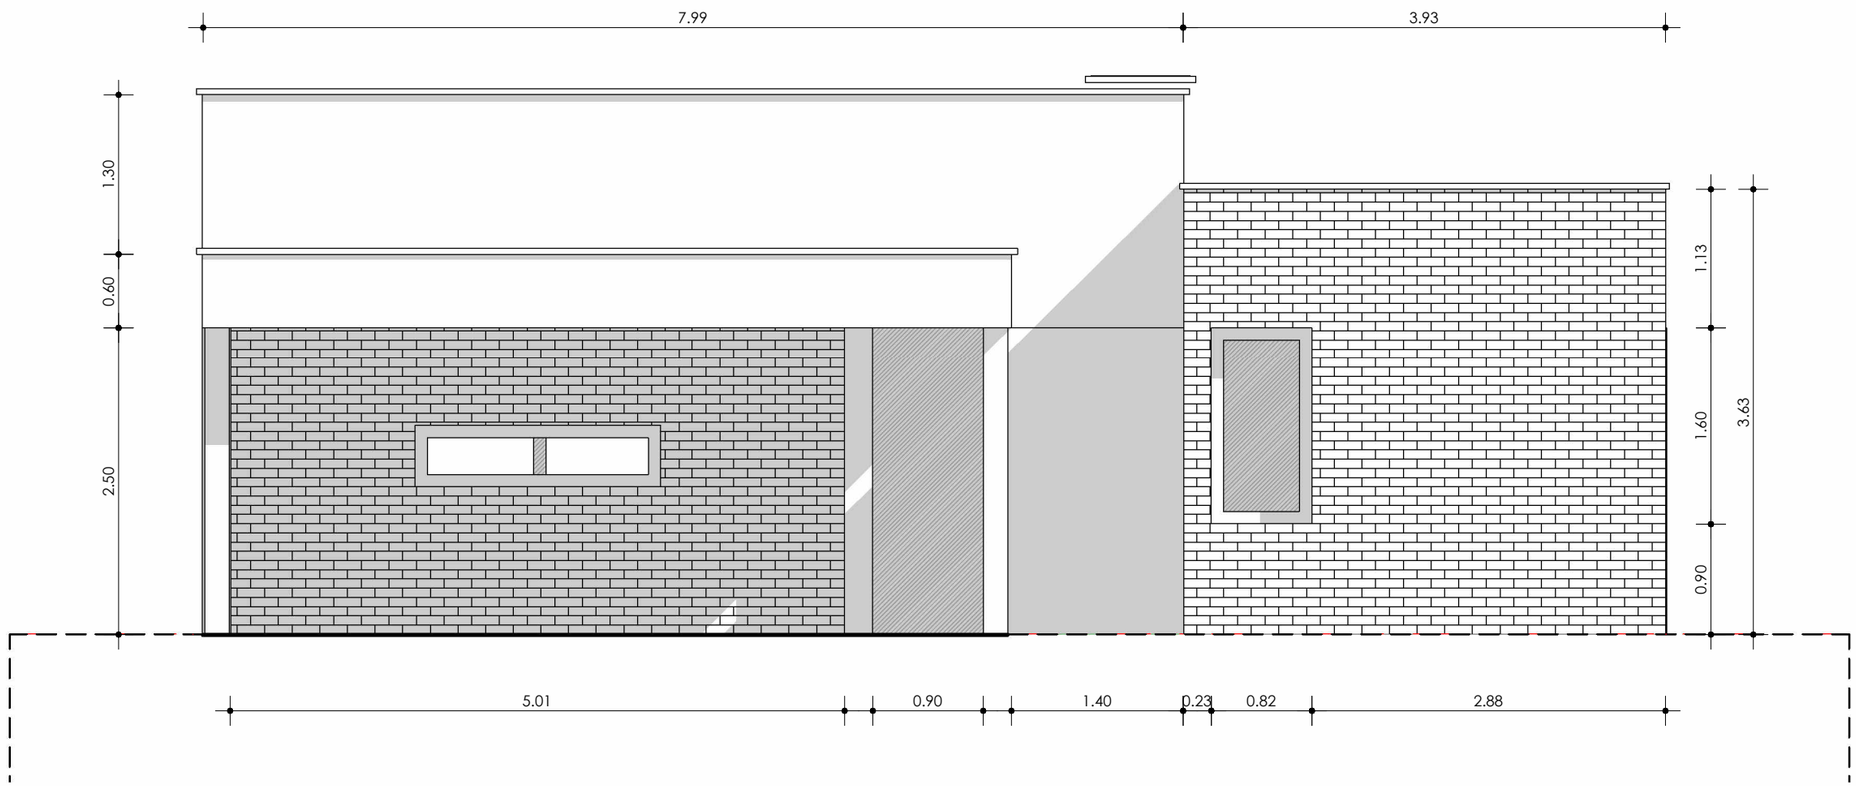


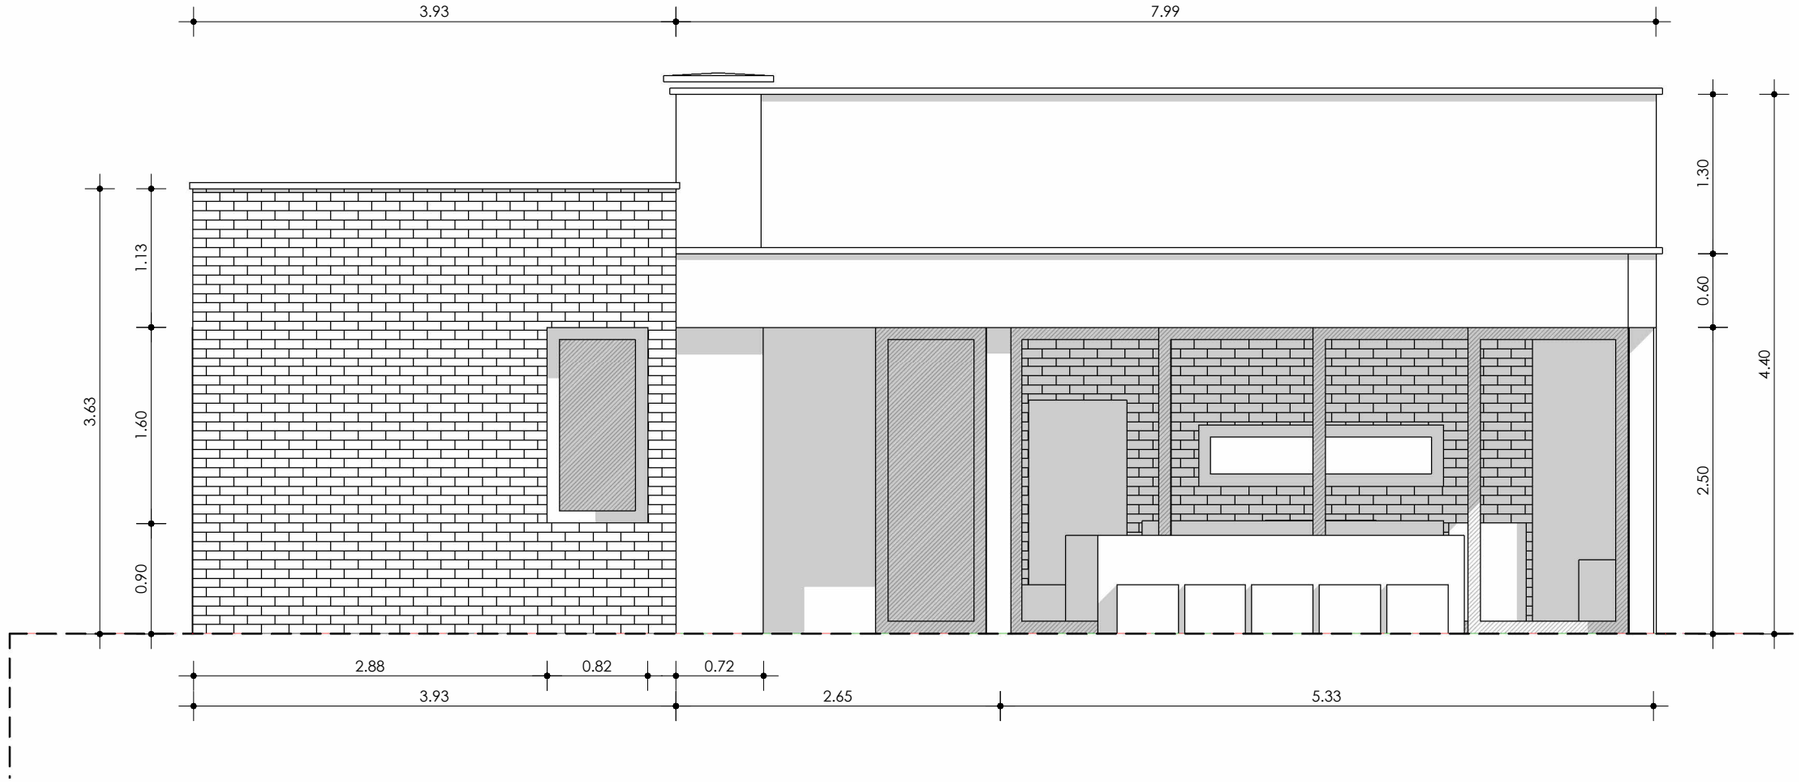


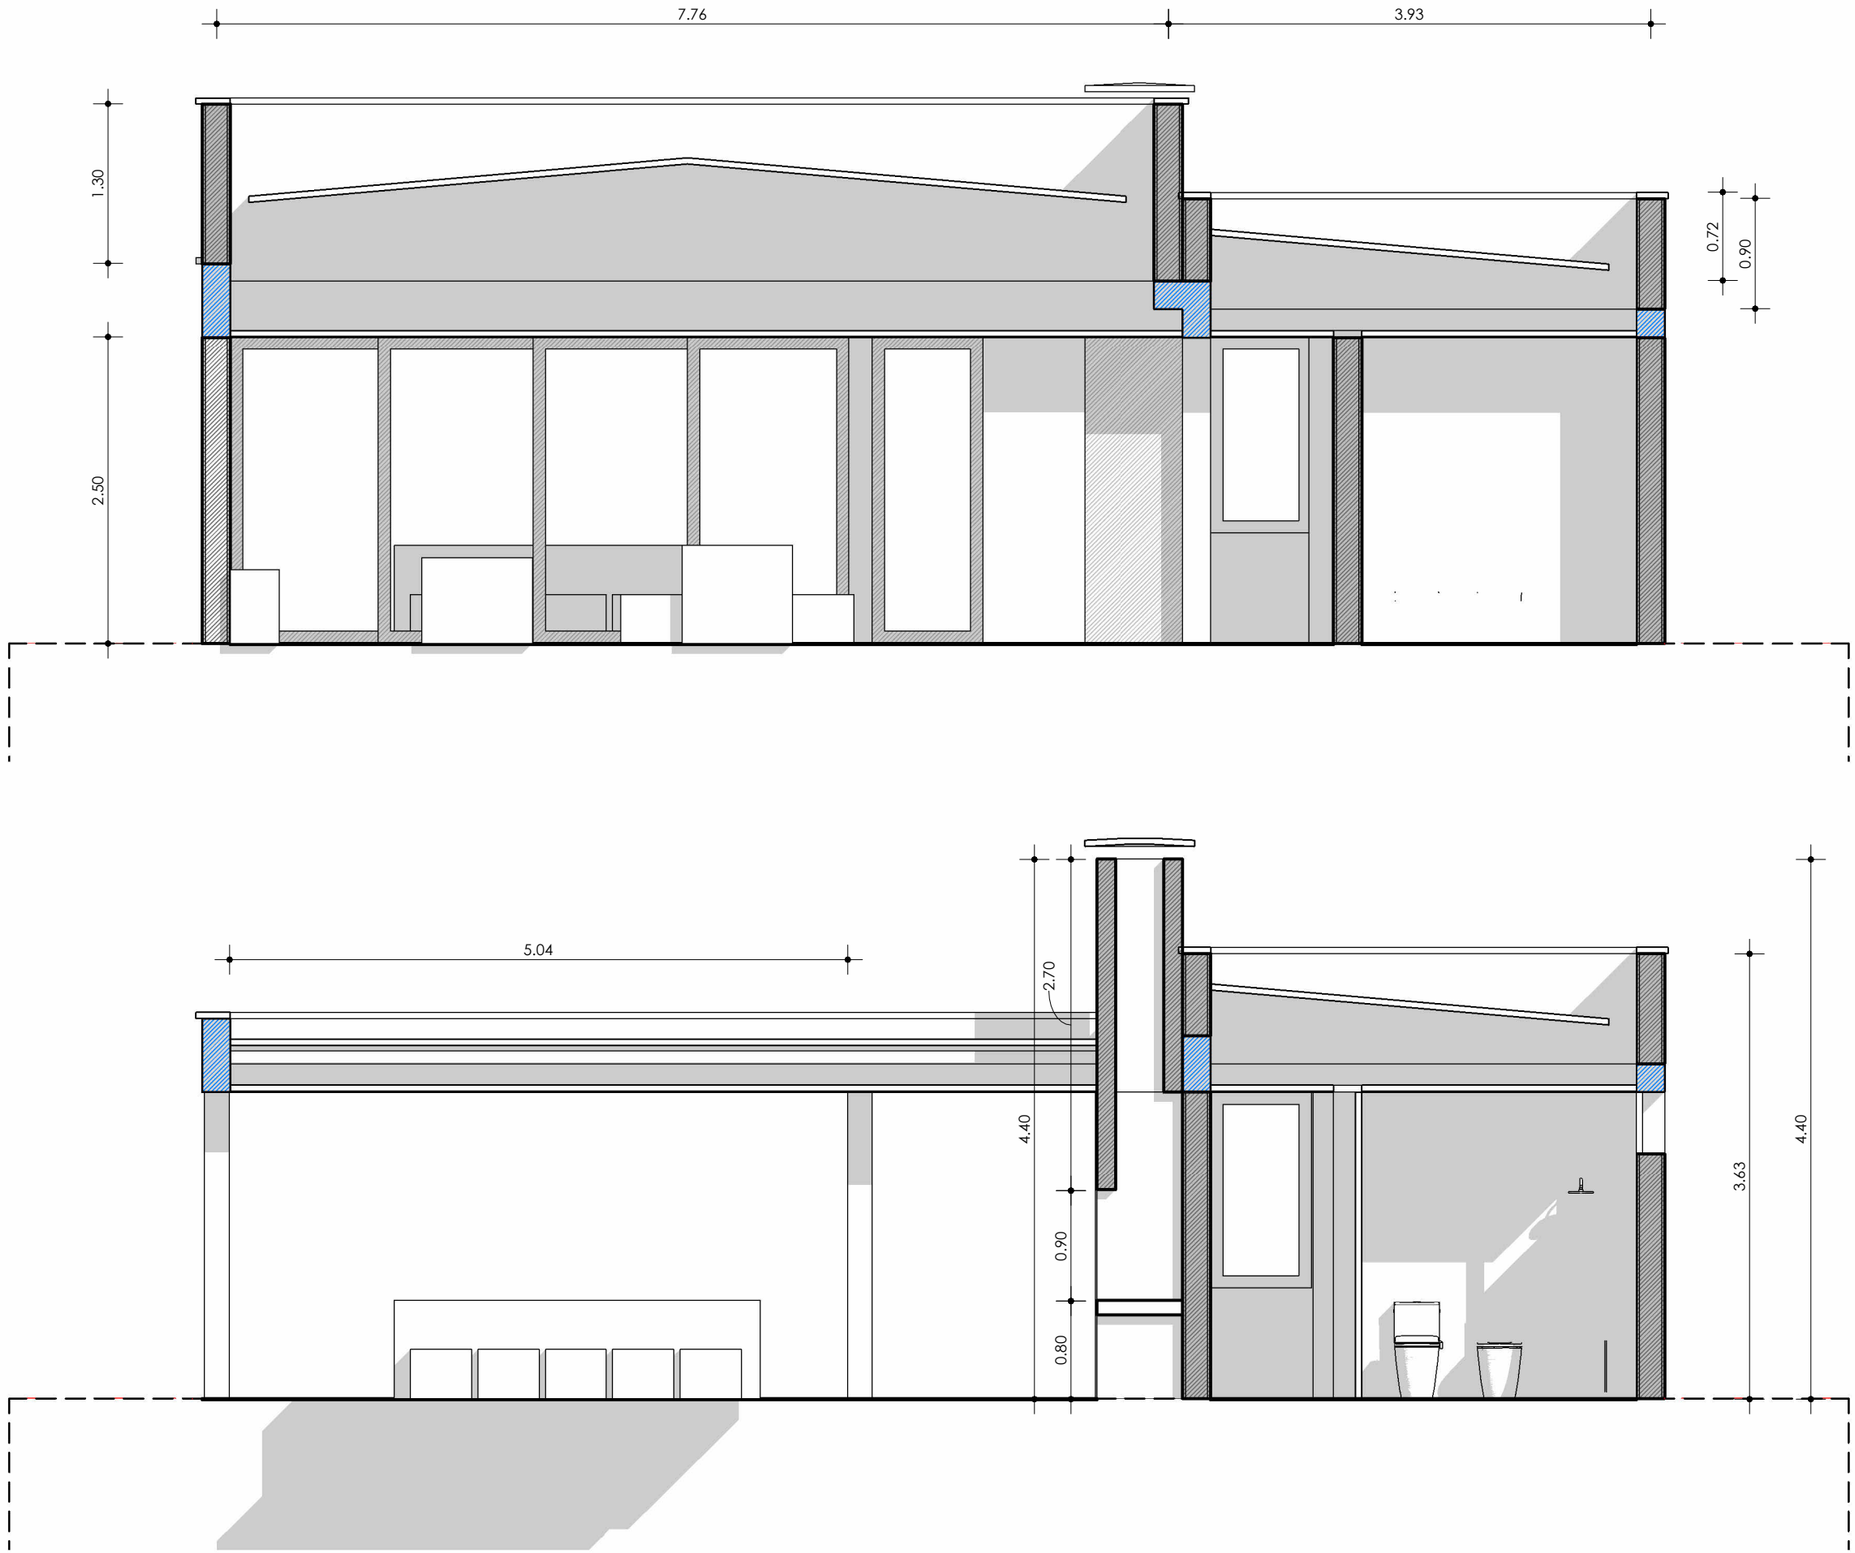
SUPERFICIE CUBIERTA: 123.20 m²
SUPERFICIE SEMICUBIERTA: 56.45 m²

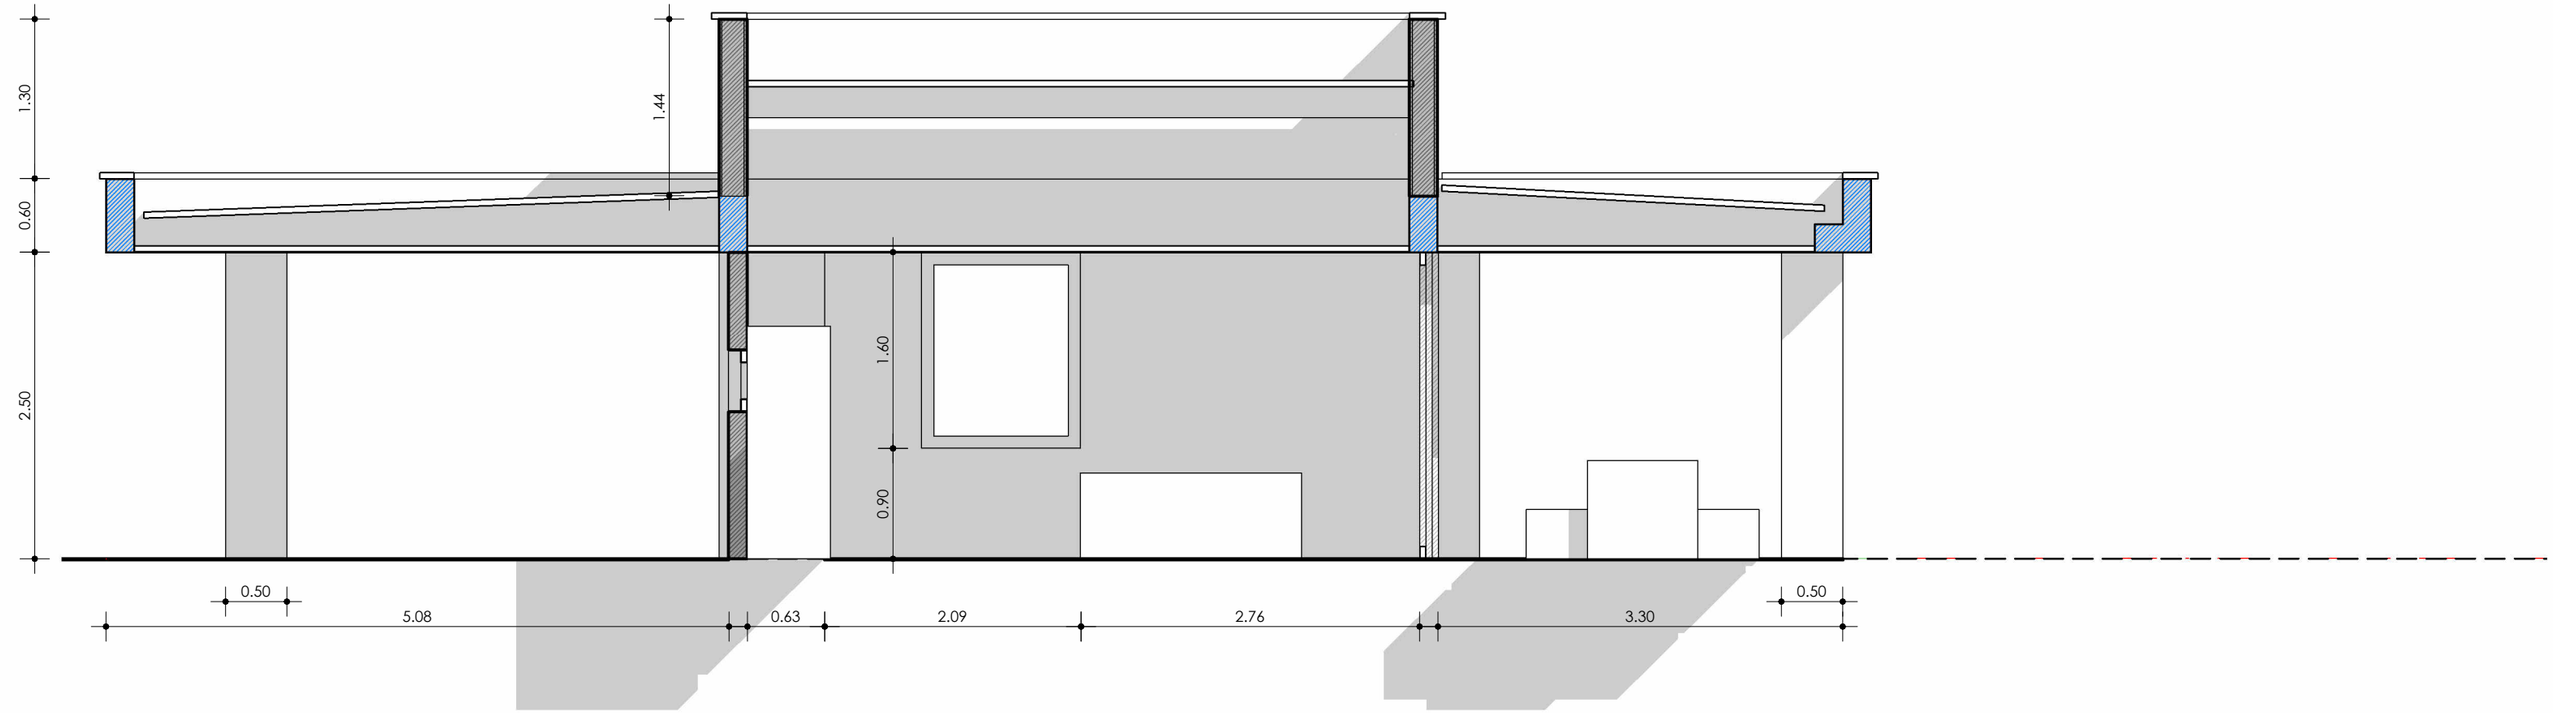
TOTAL: 179.65 m²

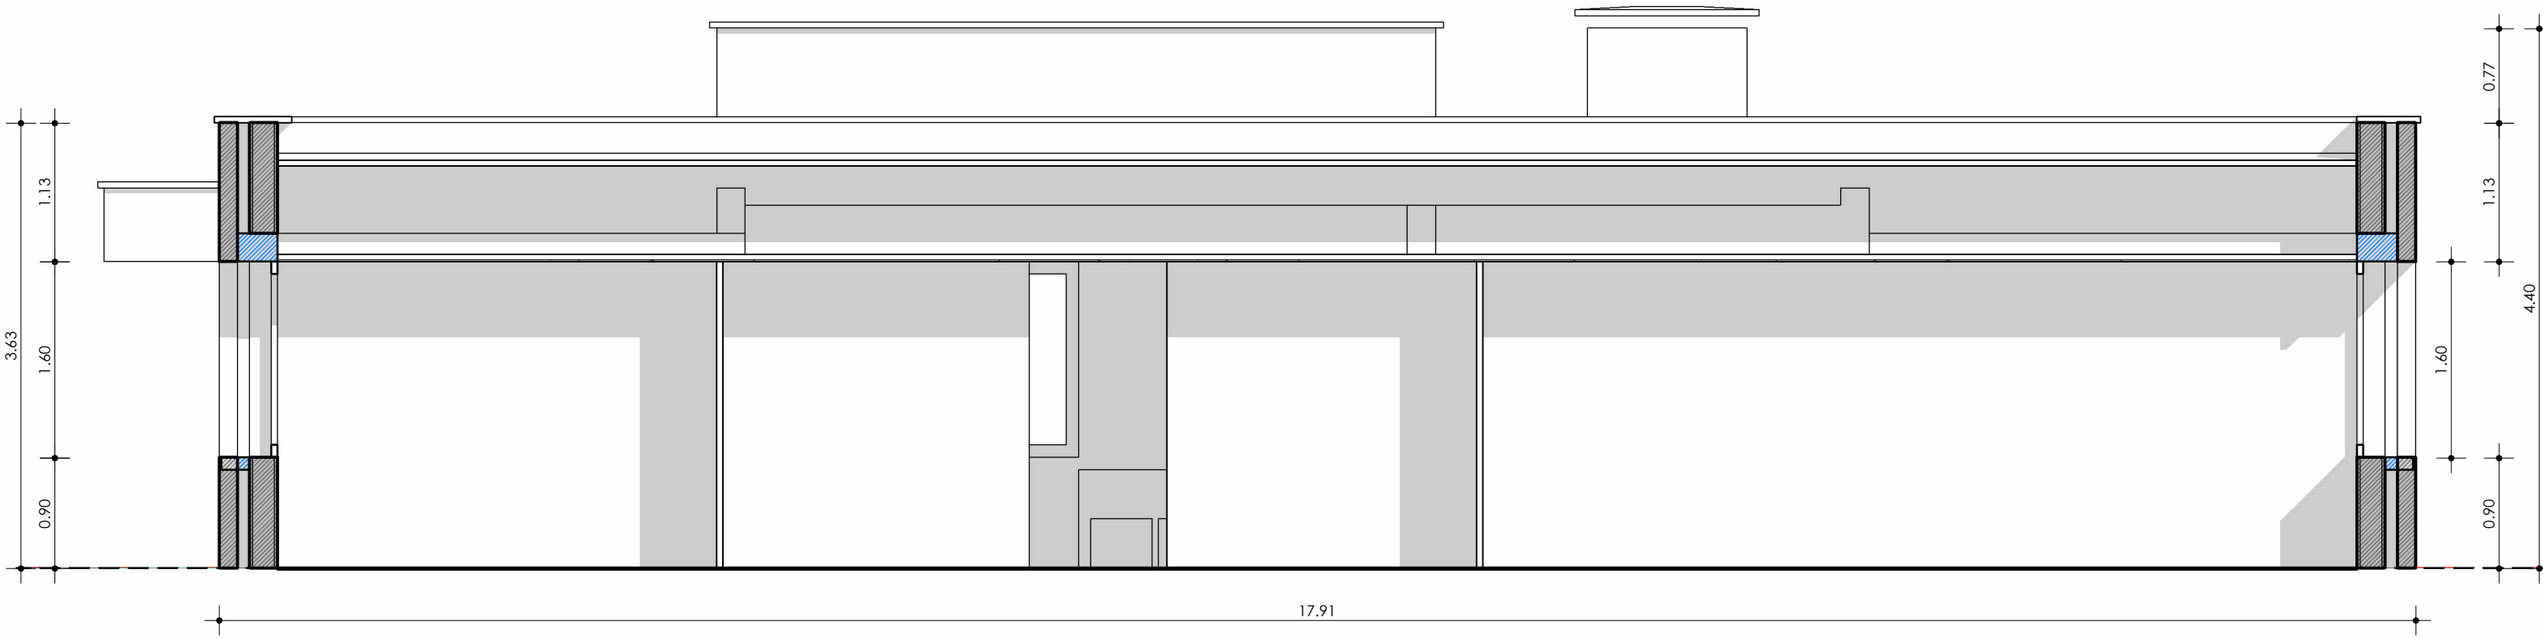
(SUPERFICIE DESCUBIERTA*: 33.18 m²)


7.99
3.93
1.30
0.60
2.50
1.13
1.60
3.63
0.90
5.01
0.90
1.40
0.23
0.82
2.88


3.93
7.99
1.13
1.60
0.90
3.63
1.30
0.60
2.50
4.40
2.88
0.82
0.72
3.93
2.65
5.33


7.76
3.93
1.30
2.50
0.72
0.90
5.04
2.70
4.40
0.90
0.80
3.63
4.40


1.30
0.60
2.50
1.44
1.60
0.90
0.50
5.08
0.63
2.09
2.76
3.30
0.50


3.63
1.13
1.60
0.90
17.91
0.77
1.13
1.60
0.90
4.40